



Republika e Kosovës

Qeveria - Vlada

Ministria e Mjedisit dhe Planifikimit Hapësinor / Ministarstv Sredine i Prstrng Planiranja
AGJENCIA KADASTRALE E KOSOVËS / KATASTARSKA AGENCIJA KOSOVA

Situacioni i terrenit

Zyra kadastrale kmunale / pëtinska katastarska kancelaria: Ferizaj

Zona kadastrale / Katastarska zona: Ferizaj

Nr. i njësisë kadastrale / Br. katastarske jedinice : 743-14

Numri i lëndës / Broj predmeta:

Shkalla e zvoglimit / Razmëra plana 1: 300

Lista e koordinatave të pikave të matura:

Nr	Y	X	H	DSC
100	7511671.585	4691921.977	616.960	100
101	7511672.448	4691927.188	616.990	101
102	7511655.190	4691922.563	616.960	102
103	7511675.256	4691951.141	616.891	103
105	7511661.931	4691974.674	616.987	105
106	7511676.006	4691955.897	616.896	106
107	7511679.020	4691970.983	616.927	107
108	7511679.172	4691972.303	616.892	108
109	7511659.987	4691957.771	616.974	109
110	7511660.700	4691962.832	616.988	110
111	7511659.451	4691952.990	617.044	111
112	7511659.885	4691958.552	616.526	112
6	7511673.903	4691936.714	617.084	BUNAR
21	7511669.780	4691956.185	617.093	FS1
17	7511665.766	4691961.650	625.621	KULMI
18	7511653.064	4691967.722	625.621	KULMI
7	7511661.125	4691961.613	617.175	KYOQE-USJELLES
1	7511661.565	4691962.832	617.239	P1
4	7511659.158	4691965.748	617.607	P4
5	7511673.444	4691965.103	617.108	P1
10	7511670.100	4691972.931	622.705	P1
302	7511674.435	4691972.390	617.607	P1
303	7511670.133	4691973.037	617.607	P1
2	7511668.606	4691961.736	617.137	P1
3	7511663.059	4691974.027	617.137	P1

Shpjegues:


- Kufiri kadastral (nga SIKTK-G)
- Rr. Ndërtesa në trajtim për legalizim
- Ndërtesa tjera
- Aneks Ndërtimi
- △ Shtyllë elektrike
- Pusetë e ujësjellësít
- Pusetë e ujërave të zeza
- Strehët
- Pikë e objekteve fqinje
- Rr. Emri i rrugës
- P1 Pikë e rrjetës gjeodezike
- 131 △ Pikë e strehëve
- 81 ● Pikë e terasës
- 10 ● Pikë e objektit
- 93 ■ Pikë e murit
- 92 ● Pikë e kulmit

Rilevoi / Snimi: LIRIDON SEJDIU
(emri dhe mbiemri i gjedjetit/kompanisë/ ime i prezime gedeta/ kompanije)

Nr. i licencës / Br. licence: 140

Data e rilevimit / Datum snimanja: 09.04.2021

Nënshkrimi / Potpis: v.v.

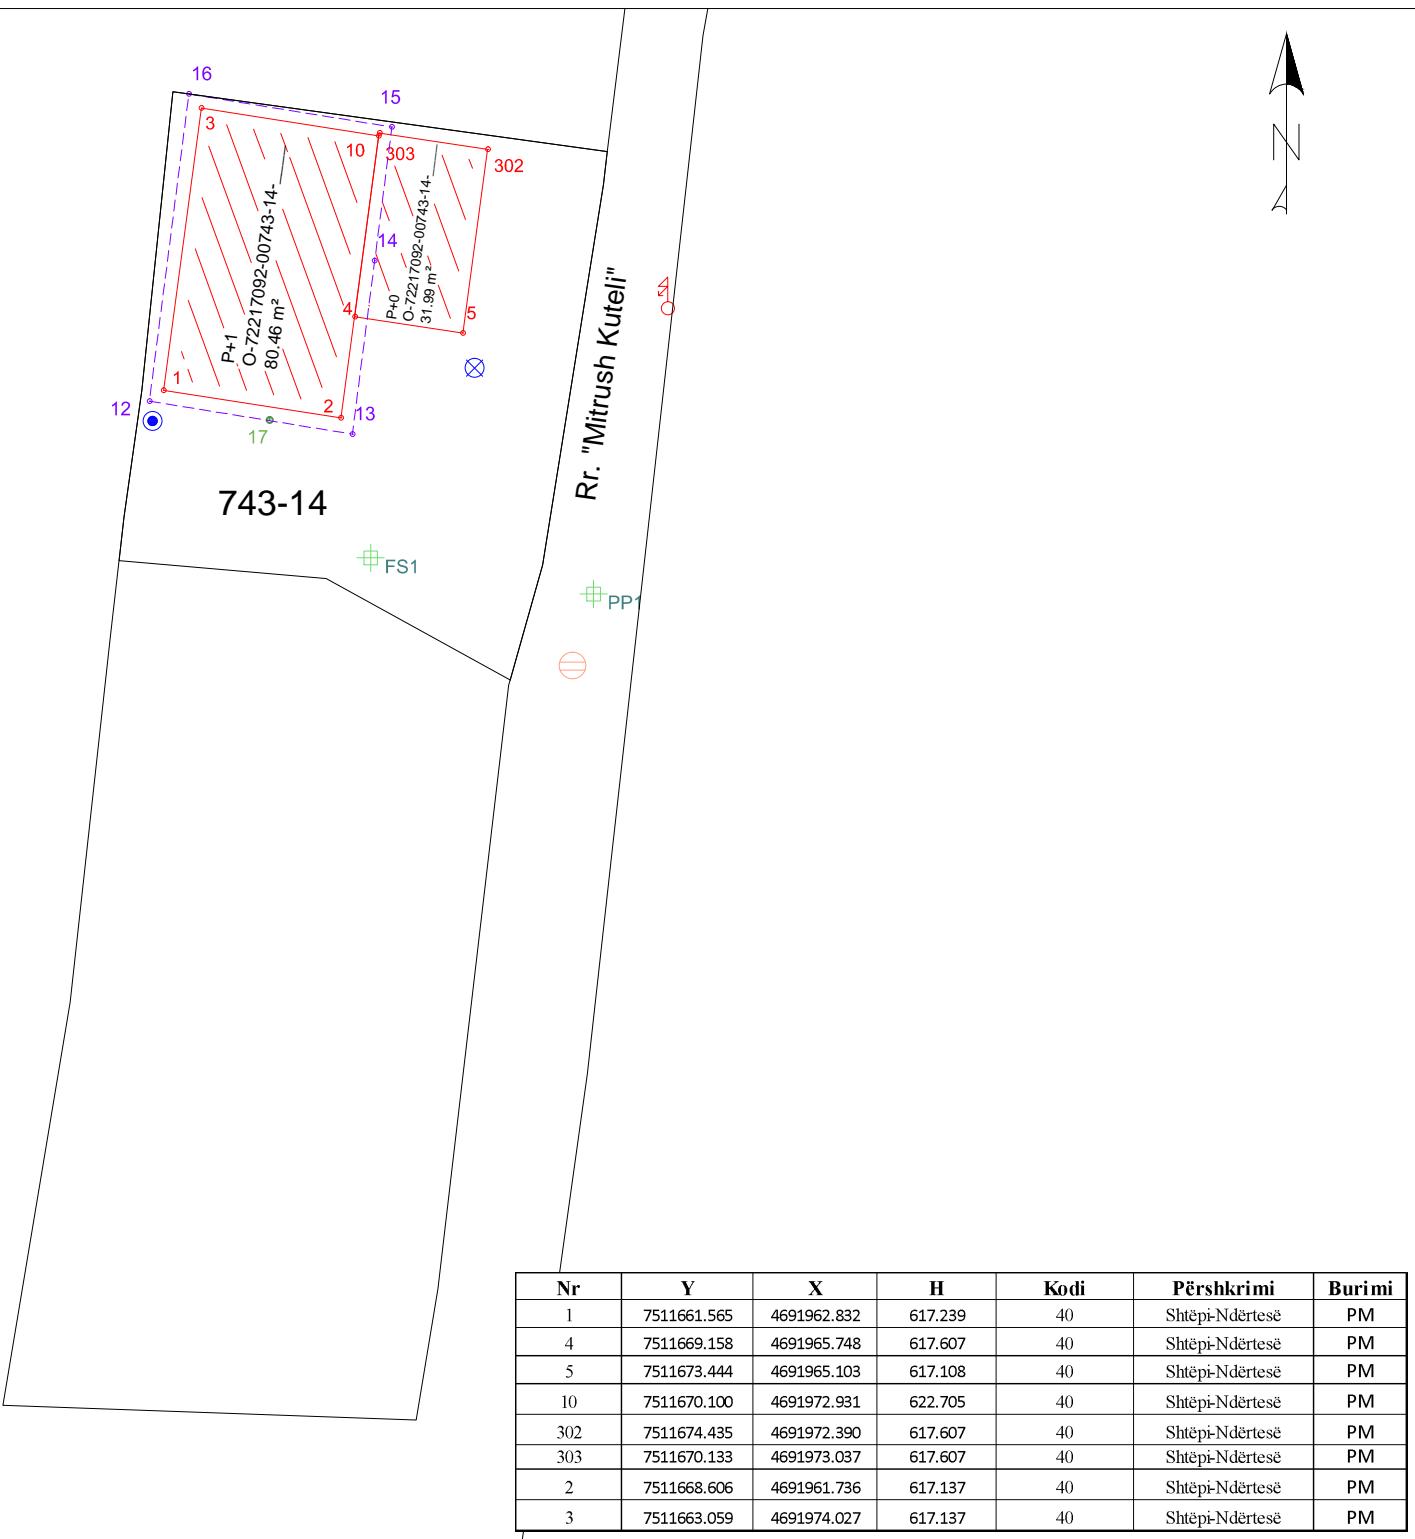



Republika e Kosovës

Qeveria - Vlada

Ministria e Mjedisit dhe Planifikimit Hapësinor / Ministerstvo Sredine i Prstrng Planiranja
AGJENCIA KADASTRALE E KOSOVËS / KATASTARSKA AGENCIJA KOSOVA

Situacioni i terrenit

Orto 2004

Ferizaj

Zyra kadastrale kmunale / pëstinska katastarska kancelaria: _____

Ferizaj

Nr. i njësisë kadastrale / Br. katastarske jedinice : _____

743-14

Numri i lëndës / Broj predmeta: _____

Shkalla e zvoglimit / Razmëra plana 1: _____

300

Lista e koordinatave të pikave të matura:

Nr	Y	X	H	DSC
100	7511671.585	4691921.977	616.960	100
101	7511672.448	4691927.188	616.990	101
102	7511655.190	4691922.563	616.960	102
103	7511675.256	4691951.143	616.891	103
105	7511661.931	4691974.674	616.987	105
106	7511676.606	4691955.897	616.896	106
107	7511679.020	4691970.983	616.927	107
108	7511679.172	4691972.303	616.892	108
109	7511659.987	4691957.771	616.974	109
110	7511660.700	4691962.832	616.988	110
111	7511659.451	4691952.990	617.044	111
112	7511659.885	4691958.552	616.526	112
6	7511673.903	4691963.714	617.084	BUNAR
21	7511669.780	4691956.185	617.093	FS1
17	7511665.766	4691961.650	625.621	KULMI
18	7511653.064	4691967.722	625.621	KULMI
7	7511661.125	4691961.613	617.175	KYQE-USJELLES
1	7511661.565	4691962.832	617.239	P1
4	7511659.158	4691965.748	617.607	P4
5	7511673.444	4691965.103	617.108	P5
10	7511670.100	4691972.931	622.705	P10
302	7511674.435	4691972.390	617.607	P302
303	7511670.133	4691973.037	617.607	P303
2	7511668.606	4691961.736	617.137	P2
3	7511663.059	4691974.027	617.137	P3

Shpjegues:

- Kufiri kadastral (nga SIKTK-G)
- Ndërtesa në trajtim për legalizim
- ▢ Ndërtesa tjera
- ▢ Aneks Ndërtimi
- ▢ Shtyllë elektrike
- Pusetë e ujësjellësít
- Pusetë e ujërave të zeza
- Strehët
- Pikë e objekteve fqinje
- Rr. Emri i rrugës
- Pikë e rrjetës gjeodezike
- Pikë e strehëve
- Pikë e terasës
- Pikë e objektit
- Pikë e murit
- Pikë e kulmit

Rilevoi / Snimi: LIRIDON SEJDIU
(emri dhe mbiemri i gjedjetit/kompanisë/ ime i prezime gedeta/ kompanije)

Nr. i licencës / Br. licence: 140

Data e rilevimit / Datum snimanja: 09.04.2021

Nënshkrimi / Potpis: _____
v.v.

Nr	Y	X	H	Kodi	Përshkrimi	Burimi
1	7511661.565	4691962.832	617.239	40	Shtëpi-Ndërtesë	PM
4	7511659.158	4691965.748	617.607	40	Shtëpi-Ndërtesë	PM
5	7511673.444	4691965.103	617.108	40	Shtëpi-Ndërtesë	PM
10	7511670.100	4691972.931	622.705	40	Shtëpi-Ndërtesë	PM
302	7511674.435	4691972.390	617.607	40	Shtëpi-Ndërtesë	PM
303	7511670.133	4691973.037	617.607	40	Shtëpi-Ndërtesë	PM
2	7511668.606	4691961.736	617.137	40	Shtëpi-Ndërtesë	PM
3	7511663.059	4691974.027	617.137	40	Shtëpi-Ndërtesë	PM



Republika e Kosovës

Qeveria -Vlada

Ministria e Mjedisit dhe Planifikimit Hapësinor /Ministarstv Sredine i Prstrng Planiranja
AGJENCIA KADASTRALE E KOSOVËS / KATASTARSKA AGENCIJA KOSOVA

Situacioni i terrenit

Orto 2018

Ferizaj

Zyra kadastrale kmunale / pëtinska katastarska kancelaria: _____

Ferizaj

Nr. i njësisë kadastrale / Br. katastarske jedinice : _____ 743-14

Numri i lëndës / Broj predmeta:

Shkalla e zvoglimit / Razmëra plana 1: _____ 300

Lista e koordinatave të pikave të matura:

Nr	Y	X	H	DSC
100	7511671.585	4691921.977	616.960	100
101	7511672.448	4691927.188	616.990	101
102	7511655.190	4691922.563	615.960	102
103	7511675.256	4691951.141	616.891	103
105	7511661.931	4691974.674	616.987	105
106	7511676.606	4691955.897	616.896	106
107	7511679.020	4691970.983	616.927	107
108	7511679.172	4691972.303	616.892	108
109	7511659.987	4691957.771	616.974	109
110	7511660.700	4691962.832	616.988	110
111	7511659.451	4691952.990	617.044	111
112	7511659.885	4691958.552	616.526	112
6	7511673.903	4691936.714	617.084	BUNAR
21	7511669.780	4691956.185	617.093	FS1
17	7511665.766	4691956.650	625.621	KULMI
18	7511653.064	4691967.722	625.621	KULMI
7	7511661.125	4691961.613	617.175	KYOQE-USJELLES
1	7511661.565	4691962.832	617.239	40
4	7511669.158	4691965.748	617.607	40
5	7511673.444	4691965.103	617.108	40
10	7511670.100	4691972.931	622.705	40
302	7511674.435	4691972.390	617.607	40
303	7511670.133	4691973.037	617.607	40
2	7511668.606	4691961.736	617.137	40
3	7511663.059	4691974.027	617.137	40

Shpjegues:

- Kufiri kadastral (nga SIKTK-G)
- Ndërtesa në trajtim për legalizim
- Ndërtesa tjera
- ▢ Aneks Ndërtimi
- ▢ Shtyllë elektrike
- Pusetë e ujësjellësít
- Pusetë e ujërave të zeza
- Strehët
- Pikë e objekteve fqinje
- Rr. Emri i rrugës
- ⊕ Plik e rrjetës gjeodezike
- 131. Pikë e strehëve
- 81. Pikë e terasës
- 10. Pikë e objektit
- 93. Pikë e murit
- 92. Pikë e kulmit

Rilevoi / Snimi: LIRIDON SEJDIU
(emri dhe mbiemri i gjedjetit/kompanisë/ ime i prezime gedeta/ kompanije)

Nr. i licencës / Br. licence: 140

Data e rilevimit / Datum snimanja: 09.04.2021

Nënshkrimi / Potpis: _____ v.v.





Republika e Kosovës
Republika Kosova-Republic of Kosovo
Qeveria e Kosovës- Vlada Kosova- Government of Kosovo
Ministria e Infrastrukturës dhe Ambientit/ Ministrastvo Infrastrukture i Sredine/ Ministry of Infrastructure and Environment
AGJENCIA KADASTRALE E KOSOVËS/KOSOVSKA KATASTARSKA AGENCIJA/ KOSOVO CADASTRAL AGENCY

Komuna: Ferizaj

Numri i njësis kadastrale: 00743-14

Zona Kadastrale: Ferizaj

Sistemi koordinat: KosovaRef01

Nr	Y	X	H	Kodi	Përshkrimi	Burimi
1	7511661.565	4691962.832	617.239	40	Shtëpi-Ndërtesë	PM
4	7511669.158	4691965.748	617.607	40	Shtëpi-Ndërtesë	PM
5	7511673.444	4691965.103	617.108	40	Shtëpi-Ndërtesë	PM
10	7511670.100	4691972.931	622.705	40	Shtëpi-Ndërtesë	PM
302	7511674.435	4691972.390	617.607	40	Shtëpi-Ndërtesë	PM
303	7511670.133	4691973.037	617.607	40	Shtëpi-Ndërtesë	PM
2	7511668.606	4691961.736	617.137	40	Shtëpi-Ndërtesë	PM
3	7511663.059	4691974.027	617.137	40	Shtëpi-Ndërtesë	PM

Gjeodeti / Kompania gjeodete e licencuar:	Liridon Sejdiu	Nënshkrimi dhe vula:	
Numri i licencës	140		

Kérko | **Rezultati i kérkimit** | **Ndihma**

Shfaq **Zgjedhur** **Rezultatet** **Sharko**

ParcelDetailId	CadastreUnitId	CadastreZoneId	CadastreZoneCode
12566832	P-72217092-00...	72217092	72

Vendos në objekt Zmadho në objekt

Numri i rezultateve: 1 (showing first 1)
Nga harta: 0

Detajet

ParcelDetailId: 12566832
CadastreUnitId: P-72217092-00743-14
CadastreZoneId: 72217092
CadastreZoneCode: 72217092
Geometry:
Status: 1
Sipërfaqja Grafike (m²): 324.8

Raport

Lista e shtresës

- Ortofoto**
 - Orthophoto2018Rural
 - Orthofoto2018Malore
 - Orthofoto2018Urban
 - Orthofoto 2015 UAV
 - Orthofoto 2012
 - Orthofoto 2009
 - Orthofoto 2004
 - Orthofoto 2001
- Rilevimi**
 - Indeksi i Ortofotove 2018
- Hartat Topografike**
 - Harta Topografike 1:25000 (2015)
 - Nomenklatura
- Rjeti Rugor**
 - Autostradë
 - Rrugë Nacionale
 - Rrugë Rajonale
- Njësia Administrative**
 - Kufin Shtetëror
 - Kufijët e Dherat e Komunave
 - Zonë urbane
- Njësia Kadastrale**
 - Zonat Kadastrale
 - Parcelat**
 - Numri parcelës
 - Ndërtesa
 - Numri ndërtesa
- Sistemi i Adresave**
 - Rugret
 - Emrat e rugëve
 - Adresa**
- Gjendja e Adresave ne Kosove**
 - Adresat në gjeoportal
 - Emërtimi i rugëve
 - Tabelat e emrave të rugëve
 - Tabelat e numrave të adresave
- Pasqyrimi i hartave kadastrale**

1 : 500

Kérko

Shfaq këshillat

Pozita: 7511684.270, 4691966.164

Zyra kadastrale komunale / Opštinska katastarska kancelarija: Ferizaj



Nr. i njësisë kadastrale / Br. katastarske jedinice : 743-14

Zona kadastrale / Katastarska zona: Ferizaj

Numri i lëndës / Broj predmeta: _____

Lloji i njësisë kadastrale / Vrsta katastarske jedinice : Shtëpi

Shkalla e zvoglimit / Razmera plana 1: 300


Republika e Kosovës

Republika Kosova-Republic of Kosovo

Qeveria -Vlada-Government

Ministria e Mjedisit dhe Planifikimit Hapësinor /Ministarstvo Sredine i Prostornog Planiranja/Ministry of Environment and Spatial Planning

AGJENCIA KADASTRALE E KOSOVËS/KATASTARSKA AGECIJA KOSOVA/KOSOVA CADASTRAL AGENCY

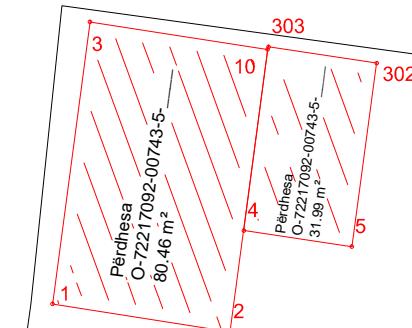

Rr. "Mitrush Kuteli"

743-14

Nr.	Y	X	H	D	Etazhi	Sqarim	Sipërfaqja (m ²)
1	7511661.57	4691962.83	617.24	PERDHESA	Përdhesa	Përdhesa 1	80.46
2	7511668.61	4691961.74	617.14	PERDHESA			
3	7511663.06	4691974.03	617.14	PERDHESA			
4	7511669.16	4691965.75	617.61	PERDHESA			
5	7511673.44	4691965.10	617.11	PERDHESA			
10	7511670.10	4691972.93	622.71	PERDHESA	Përdhesa 2	31.99	Gjithsej:
302	7511674.43	4691972.39	617.61	PERDHESA			
303	7511670.13	4691973.04	617.61	PERDHESA			112.45

Rilevoi / Snimio: LIRIDON SEJDIU
(emri dhe mbiemri i gjykozit/kompanisë/ ime i prezime geodeta/ kompanije)

Aprovoi / Usvojio: _____
(emri dhe mbiemri i pësonit zyrtar/ ime i prezime sluzbeneg lica)

Nr. i licencës / Br. licence: 140

V.V.

Nënshkrimi / Potpis: _____

Nënshkrimi / Potpis: _____

Data e rilevimit / Datum snimanja: 09.04.2021

Data e rilevimit / Datum snimanja: _____

Zyra kadastrale komunale / Opštinska katastarska kancelarija: Ferizaj



Nr. i njësisë kadastrale / Br. katastarske jedinice : 743-14

Zona kadastrale / Katastarska zona: Ferizaj

Numri i lëndës / Broj predmeta: _____

Lloji i njësisë kadastrale / Vrsta katastarske jedinice : Shtëpi

Shkalla e zvoglimit / Razmera plana 1: 300


Republika e Kosovës

Republika Kosova-Republic of Kosovo

Qeveria -Vlada-Government

Ministria e Mjedisit dhe Planifikimit Hapësinor /Ministarstvo Sredine i Prostornog Planiranja/Ministry of Environment and Spatial Planning

AGJENCIA KADASTRALE E KOSOVËS/ KATASTARSKA AGECIJA KOSOVA/ KOSOVA CADASTRAL AGENCY

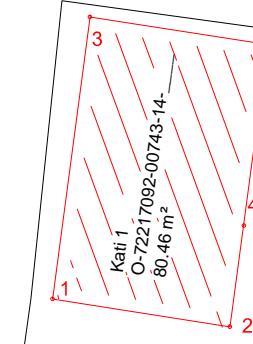

Rr. "Mitrush Kuteli"

743-14

Nr.	Y	X	H	D	Etazhi	Sqarim	Sipërfaqja (m ²)
1	7511661.57	4691962.83	620.12	Kati 1	Kati 1	Kati 1	80.46
2	7511668.61	4691961.74					
3	7511663.06	4691974.03					
4	7511669.16	4691965.75					
10	7511670.10	4691972.93					Gjithej: 80.46

Rilevoi / Snimio: LIRIDON SEJDIU
(emri dhe mbiemri i gjydetit/kompanisë/ ime i prezime geodeta/ kompanije)

Aprovoi / Usvojio: _____
(emri dhe mbiemri i pësonit zyrtar/ ime i prezime sluzbeneg lica)

Nr. i licencës / Br. licence: 140

V.V.

Nënshkrimi / Potpis: _____

Nënshkrimi / Potpis: _____

Data e rilevimit / Datum snimanja: 09.04.2021

Data e rilevimit / Datum snimanja: _____



Republika e Kosovës

Republika Kosova-Republic of Kosovo

Qeveria e Kosovës- Vlada Kosova- Government of Kosovo

Ministria e Infrastrukturës dhe Ambientit/ Ministrastvo Infrastrukture i Sredine/ Ministry of Infrastructure and Environment
AGJENCIA KADASTRALE E KOSOVËS/KOSOVSKA KATASTARSKA AGENCIJA/ KOSOVO CADASTRAL AGENCY

Komuna: Ferizaj
Numri i njësisë kadastrale: 0743-14

Zona Kadastrale: Ferizaj
Sistemi koordinat: KosovaRef01

Nr.	Y	X	H	D	Etazhi	Sqarim	Sipërfaqja (m ²)
1	7511661.57	4691962.83	617.24	PERDHESA	Përdhesa	Përdhesa 1	80.46
2	7511668.61	4691961.74	617.14	PERDHESA			
3	7511663.06	4691974.03	617.14	PERDHESA		Përdhesa 2	31.99
4	7511669.16	4691965.75	617.61	PERDHESA			
5	7511673.44	4691965.10	617.11	PERDHESA		Gjithsej:	112.45
10	7511670.10	4691972.93	622.71	PERDHESA			
302	7511674.43	4691972.39	617.61	PERDHESA			
303	7511670.13	4691973.04	617.61	PERDHESA			

Nr.	Y	X	H	D	Etazhi	Sqarim	Sipërfaqja (m ²)
1	7511661.57	4691962.83	620.12	Kati 1	Kati 1	Kati 1	80.46
2	7511668.61	4691961.74					
3	7511663.06	4691974.03					
4	7511669.16	4691965.75					
10	7511670.10	4691972.93			Gjithej:		80.46


Gjeodeti / Kompania gjeodete e licencuar:	Liridon Sejdiu	Nënshkrimi dhe vula:	
Numri i licencës	140		

Zona kadastrale / Katastarska zona: Ferizaj

Numri i lëndës / Broj predmeta: _____

Lloji i njësisë kadastrale / Vrsta katastarske jedinice : Shtëpi**Republika e Kosovës****Republika Kosova-Republic of Kosovo****Qeveria -Vlada-Government****Ministria e Mjedisit dhe Planifikimit Hapësinor /Ministarstvo Sredine i Prostornog Planiranja/Ministry of Environment and Spatial Planning**

AGJENCIA KADASTRALE E KOSOVËS/ KATASTARSKA AGECIJA KOSOVA/ KOSOVA CADASTRAL AGENCY

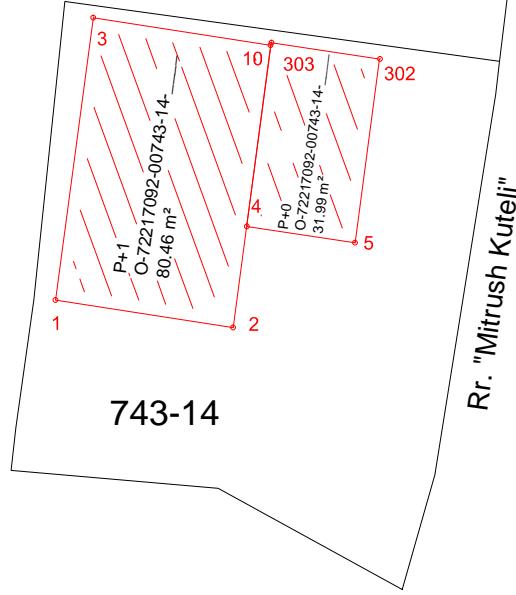

Nr	Y	X	H	Kodi	Përshkrimi	Burimi
1	7511661.565	4691962.832	617.239	40	Shtëpi-Ndërtesë	PM
4	7511669.158	4691965.748	617.607	40	Shtëpi-Ndërtesë	PM
5	7511673.444	4691965.103	617.108	40	Shtëpi-Ndërtesë	PM
10	7511670.100	4691972.931	622.705	40	Shtëpi-Ndërtesë	PM
302	7511674.435	4691972.390	617.607	40	Shtëpi-Ndërtesë	PM
303	7511670.133	4691973.037	617.607	40	Shtëpi-Ndërtesë	PM
2	7511668.606	4691961.736	617.137	40	Shtëpi-Ndërtesë	PM
3	7511663.059	4691974.027	617.137	40	Shtëpi-Ndërtesë	PM

Rilevoi / Snimio: FITORI LIPOVICA
(emri dhe mbiemri i gjyqetarit/kompanisë/ ime i prezime geodeta/ kompanije)Aprovoi / Usvojio: _____
(emri dhe mbiemri i pësonit zyrtar/ ime i prezime sluzbeneg lica)Nr. i licencës / Br. licence: 168

V.V.

Nënshkrimi / Potpis: _____

Nënshkrimi / Potpis: _____

Data e rilevimit / Datum snimanja: 10.10.2020

Data e rilevimit / Datum snimanja: _____



Republika e Kosovës

Republika Kosova - Republic of Kosovo

Qeveria e Kosovës - Vlada Kosova - Government of Kosovo

Ministria e Infrastrukturës dhe Ambientit/ Ministrastvo Infrastrukture i Sredine/ Ministry of Infrastructure and Environment

AGJENCIA KADASTRALE E KOSOVËS/ KOSOVSKA KATASTARSKA AGENCIJA/ KOSOVA CADASTRAL AGENCY

R E G J I S T R I M I I NDERTESËS / SHTËPISË													
Nr	Komuna	Zona Kadastrale	Numri i ndërtesës (njësia)	Etazhiteti	Katet	Sipërfaqja e kateve [m ²]	Sipërfaqja e bazamentit [m ²]	Adresa e Njësisë	Vendi i quajtur	Shfrytëzimi i aktual	Pronari / Shfrytëzuesi Emri (Emri i prindit) Mbiemri	Numri përsoneal	Pjesa e Pronës
1	Ferizaj	Ferizaj	O-72217092-00743-14-____-__	P+1	Përdhesa	80.46	80.46	Rr. "Mitrush Kurteli"	SARAISHTE	Afarizëm/Banim	Fahrije (Qazim) Bakija	1004518183	1/1
					Kati 1	80.46							
					Gjithsej:	160.92							

R E G J I S T R I M I I NDERTESËS / SHTËPISË													
Nr	Komuna	Zona Kadastrale	Numri i ndërtesës (njësia)	Etazhiteti	Katet	Sipërfaqja e kateve [m ²]	Sipërfaqja e bazamentit [m ²]	Adresa e Njësisë	Vendi i quajtur	Shfrytëzimi i aktual	Pronari / Shfrytëzuesi Emri (Emri i prindit) Mbiemri	Numri përsoneal	Pjesa e Pronës
1	Ferizaj	Ferizaj	O-72217092-00743-14-____-__	P+0	Përdhesa	31.99	31.99	Rr. "Mitrush Kurteli"	SARAISHTE	Afarizëm/Banim	Fahrije (Qazim) Bakija	1004518183	1/1
					Gjithsej:	31.99							

Gjeodeti/kompania e licencuar: LIRIDON SEJDIU

Nr i licencës: 140

Nënshkrimi dhe vula:







