Zyra kadastrale komunale / Opštinska katastarska kancelarija: Ferizaj

Nr. i njësisë kadastrale / Br. katastarske jedinice : 743-14

Zona kadastrale / Katastarska zona: Ferizaj

Numri i lëndës / Broj predmeta:

Lloji i njësisë kadastrale / Vrsta katastarske jedinice : Shtëpi

Shkalla e zvoglimit / Razmera plana 1: 300

Republika e Kosovës

Republika Kosova-Republic of Kosova

Qeveria -Vlada-Government

Ministria e Mjedisit dhe Planifikimit Hapësinor /Ministarstvo Sredine i Prostornog Planiranja/Ministry of Environment and Spatial Planning

AGJENCIA KADASTRALE E KOSOVËS/ KATASTARSKA AGECIJA KOSOVA/ KOSOVA CADASTRAL AGENCY

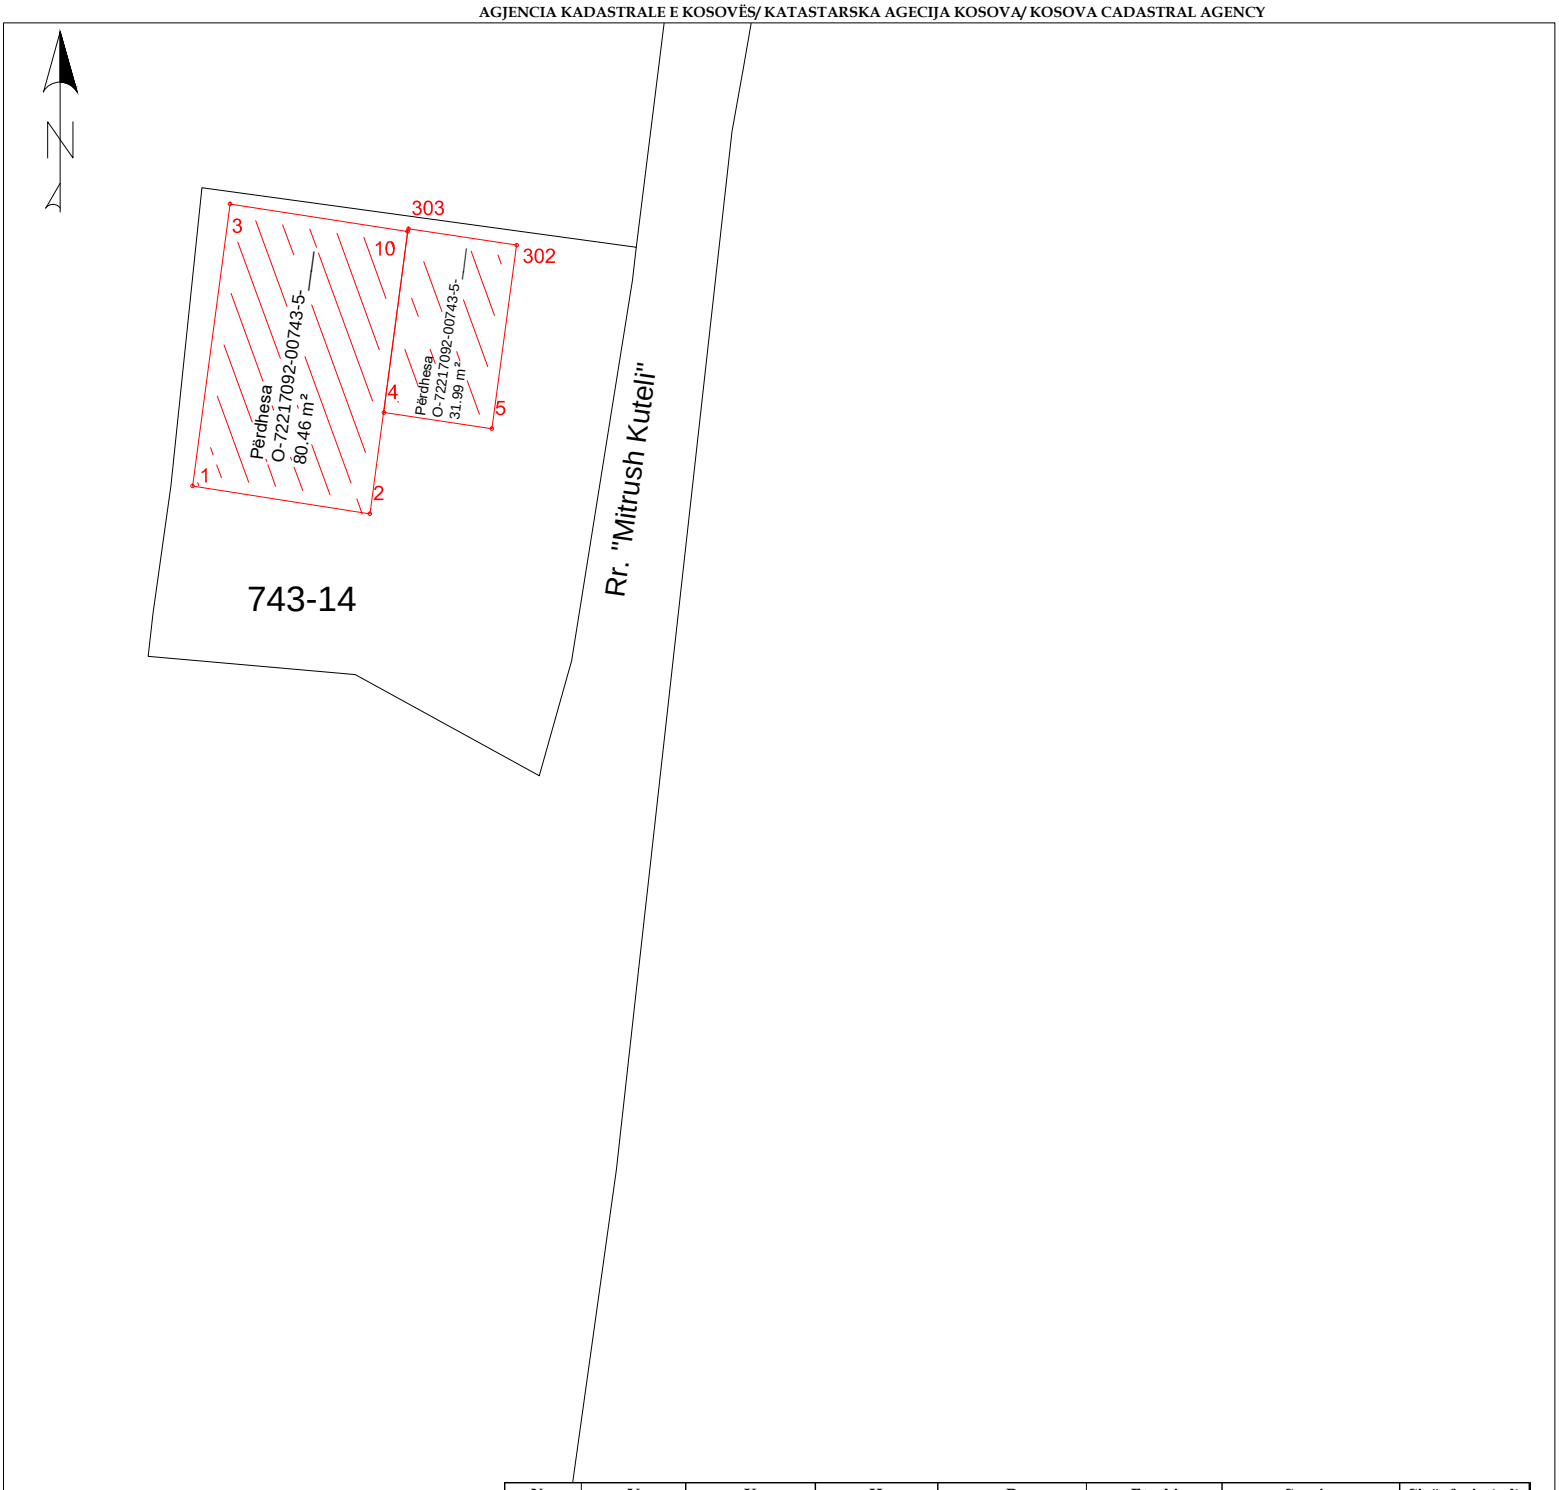

Nr.	Y	X	H	D	Etazhi	Sqarim	Sipërfaqja (m²)
1	7511661.57	4691962.83	617.24	PERDHESA	Përdhesa	Përdhesa 1	80.46
2	7511668.61	4691961.74	617.14	PERDHESA			
3	7511663.06	4691974.03	617.14	PERDHESA			
4	7511669.16	4691965.75	617.61	PERDHESA			
5	7511673.44	4691965.10	617.11	PERDHESA		Përdhesa 2	31.99
10	7511670.10	4691972.93	622.71	PERDHESA			
302	7511674.43	4691972.39	617.61	PERDHESA			
303	7511670.13	4691973.04	617.61	PERDHESA		Gjithsej:	112.45

Rilevoi / Snimio: LIRIDON SEJDIU

(emri dhe mbiemri i gjeodetit/kompanisë/ ime i prezime geodeta/ kompanije)

Nr. i licencës / Br. licence: 140

Nënshkrimi / Potpis:

Data e rilevimit / Datum snimanja: 09.04.2021

V.V.

Aprovoi / Usvojio:

(emri dhe mbiemri i përsonit zyrtar/ ime i prezime sluzbenog lica)

Nënshkrimi / Potpis:

Data e rilevimit / Datum snimanja: